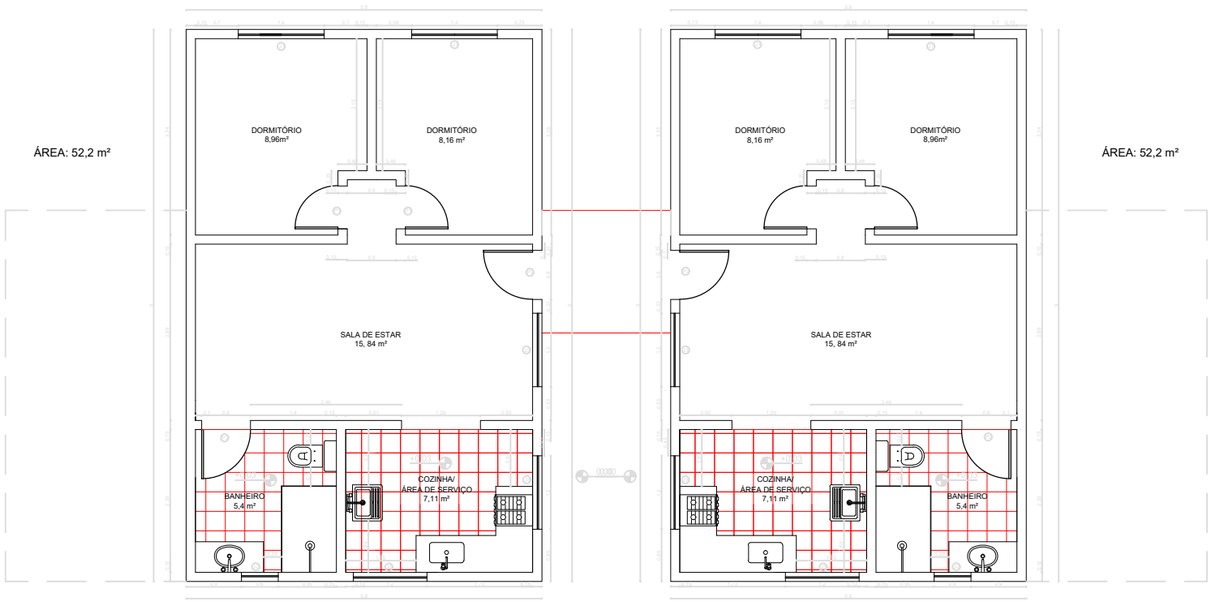

PLANTA BAIXA - TÉRREO
ESCALA 1:100

QUADRO GERAL DE ESQUADRIAS							
TIPO DE ESQUADRIA	CÓDIGO	LARGURA	ALTURA	PEITORIL	TIPO	MATERIAL	QUANTIDADE
PORTA	P1	0,7	2,1	*	ABRIR	MADEIRA	6
	P2	0,8	2,1	*	ABRIR	MADEIRA	6
JANELA	J1	1,4	1,2	1	CORRER	ALUMÍNIO	12
	J2	0,6	0,6	1,8	BASCULANTE	ALUMÍNIO	8
	J3	1,2	1,2	1	CORRER	ALUMÍNIO	16

HABITAÇÃO DE INTERESSE SOCIAL

ALUNOS:	MATRÍCULA:	PROFESSOR:		
BRUNO_DUARTE	82661	MARISTELA_SIOLARI		
		ESCALA: 1:100	PADRAO: A3	DATA: 12/20