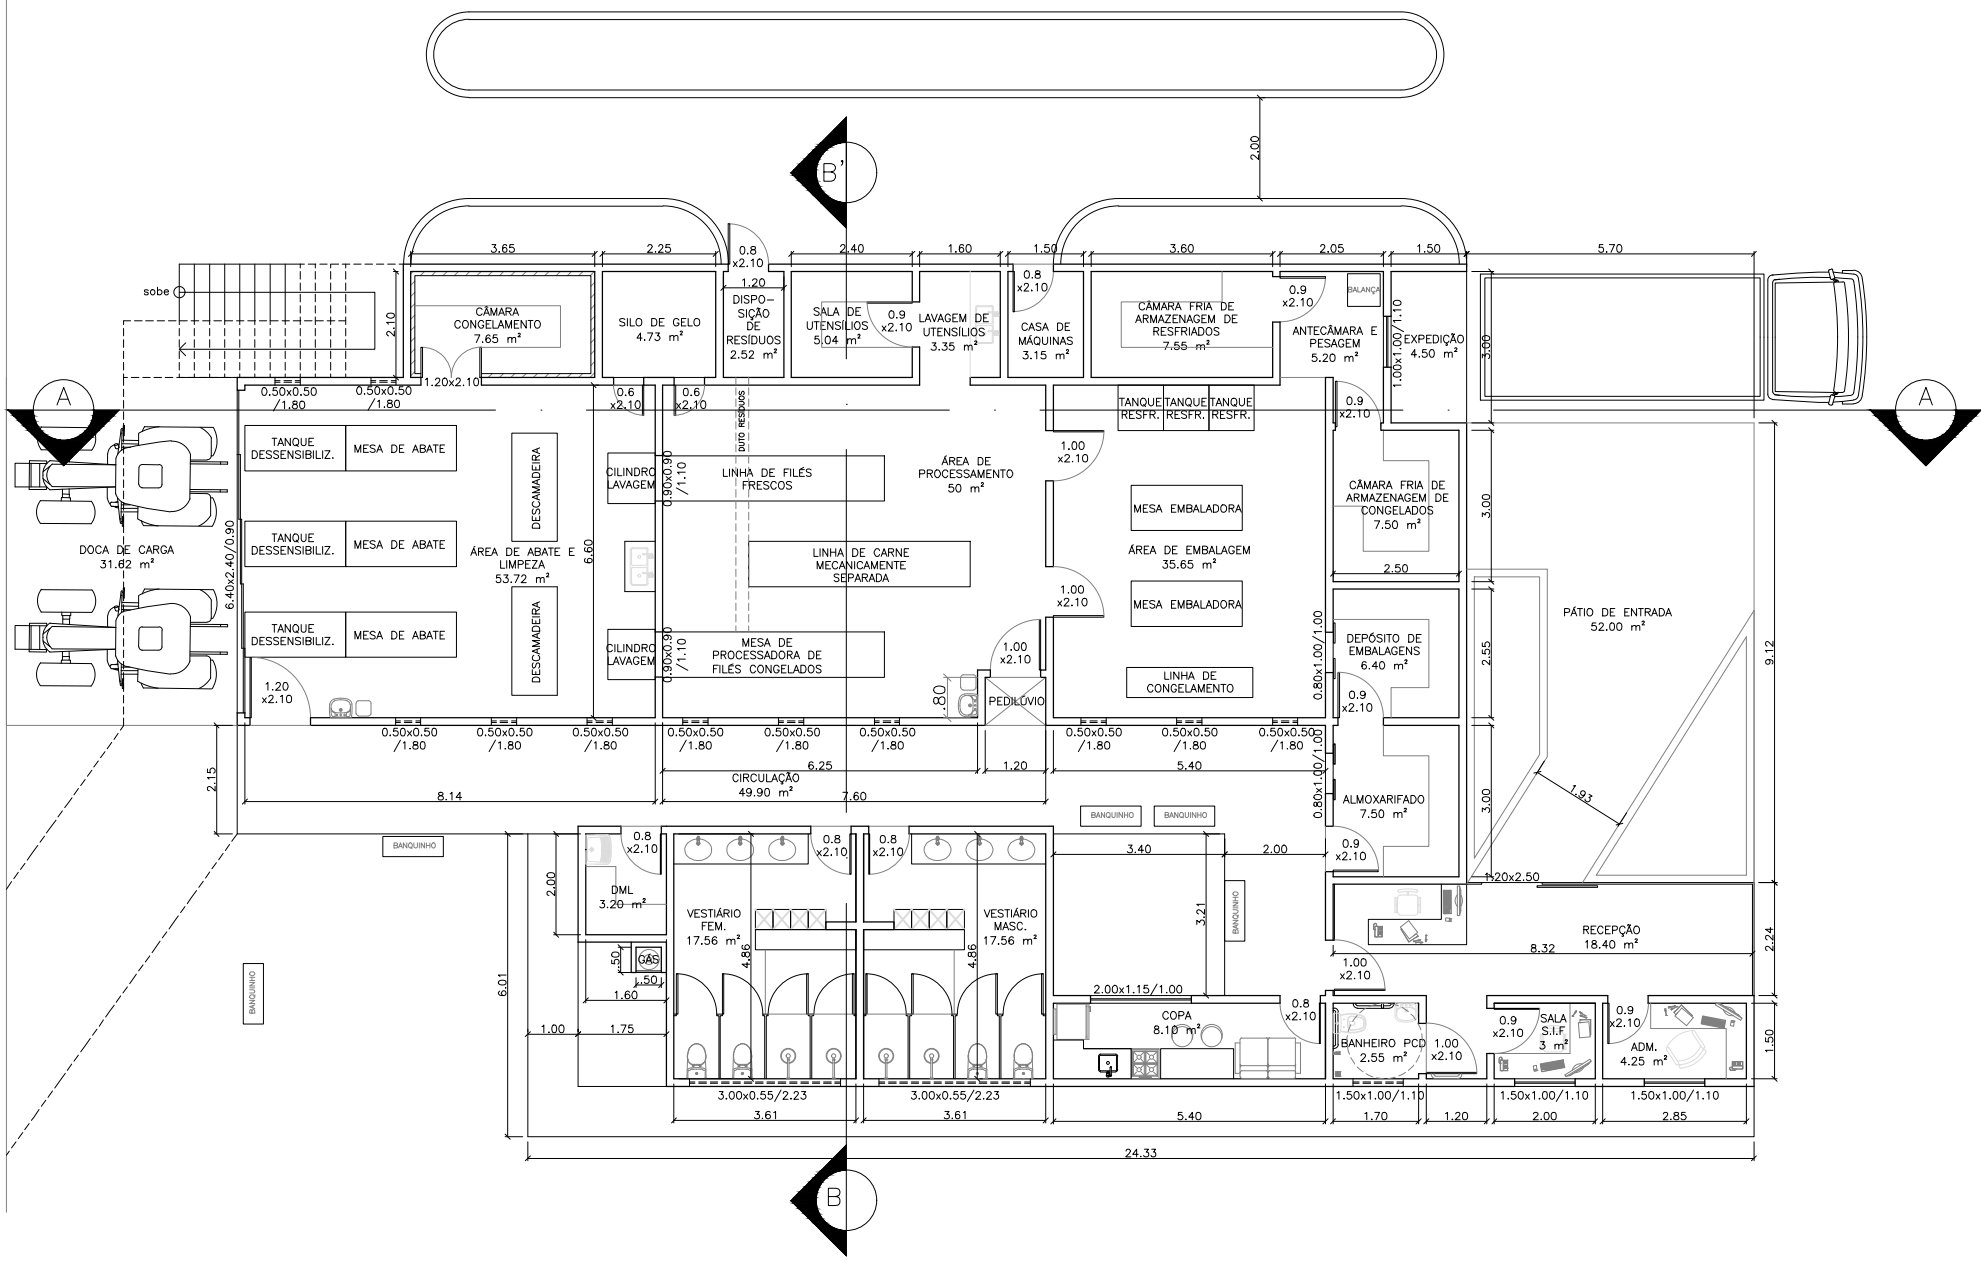
B'
B
A
A
sobe
CÂMARA CONGELAMENTO 7.65 m²
SILO DE GELO 4.73 m²
DISPO-SIÇÃO DE RESÍDUOS 2.52 m²
SALA DE UTENSÍLIOS 5.04 m²
LAVAGEM DE UTENSÍLIOS 3.35 m²
CASA DE MÁQUINAS 3.15 m²
CÂMARA FRIA DE ARMAZENAGEM DE RESFRIADOS 7.55 m²
ANTECÂMARA E PESAGEM 5.20 m²
EXPEDIÇÃO 4.50 m²
BALANÇA
DOCA DE CARGA 31.62 m²
TANQUE DESSENSIBILIZ.
MESA DE ABATE
DESCAMADEIRA
ÁREA DE ABATE E LIMPEZA 53.72 m²
CILINDRO LAVAGEM
LINHA DE FILÉS FRESCOS
DUTO RESÍDUOS
ÁREA DE PROCESSAMENTO 50 m²
LINHA DE CARNE MECANICAMENTE SEPARADA
MESA DE PROCESSADORA DE FILÉS CONGELADOS
PEDILÚVIO
TANQUE RESFR.
MESA EMBALADORA
ÁREA DE EMBALAGEM 35.65 m²
LINHA DE CONGELAMENTO
CÂMARA FRIA DE ARMAZENAGEM DE CONGELADOS 7.50 m²
DEPÓSITO DE EMBALAGENS 6.40 m²
ALMOXARIFADO 7.50 m²
PÁTIO DE ENTRADA 52.00 m²
CIRCULAÇÃO 49.90 m²
BANQUINHO
DML 3.20 m²
GÁS
VESTIÁRIO FEM. 17.56 m²
VESTIÁRIO MASC. 17.56 m²
COPA 8.10 m²
BANHEIRO PCD 2.55 m²
SALA S.I.F. 3 m²
ADM. 4.25 m²
RECEPÇÃO 18.40 m²
24.33
desce
8.15x1.25/1.05
7.60x1.25/1.05
5.40x1.25/1.05
CIRCULAÇÃO 168 m²